


Sample Window Plan - Floor 1

Demo Project | 123 Example Street

C1 - Living Room Sliding Door


Profile: Panoramic Sliding Door / Tianyu 200

Glass: 6+18A+6 Tempered White Glass

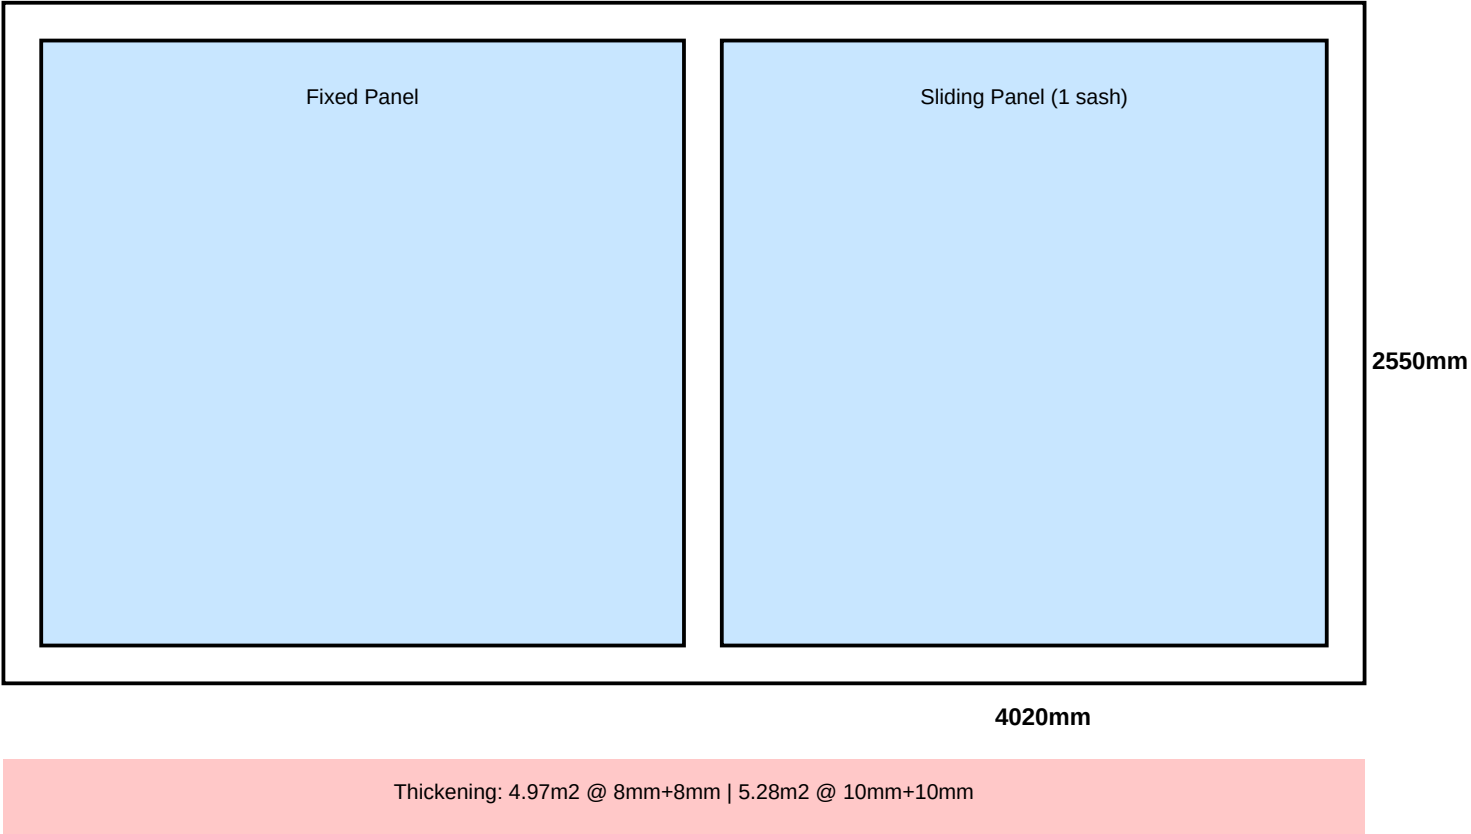

C2 - Kitchen Window

Profile: An'Neng Sliding Window | Glass: 6+18A+6

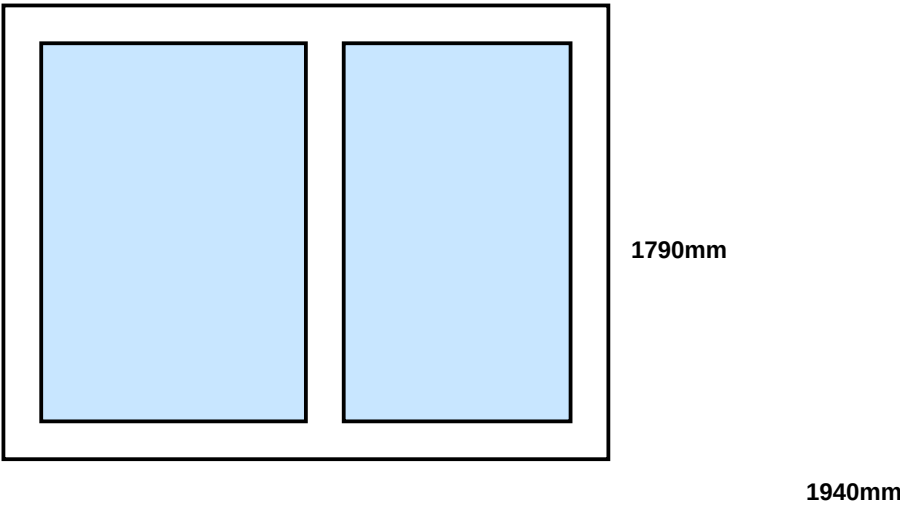


Sample Window Plan - Floor 2

Demo Project | 123 Example Street

C3 - Master Bedroom Window

Profile: S97 Inward Tilt-Turn | Glass: 6+18A+6

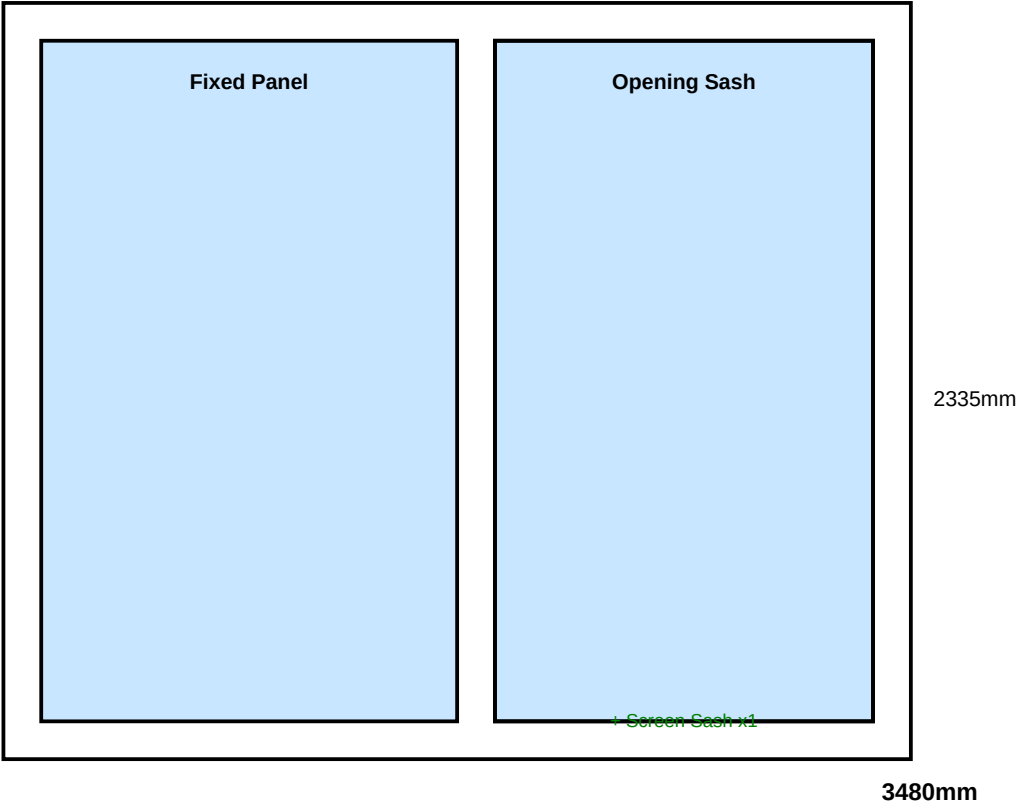

C4 - Children's Room Window

Profile: 120 Series Pressure Door | Glass: 6+18A+6

